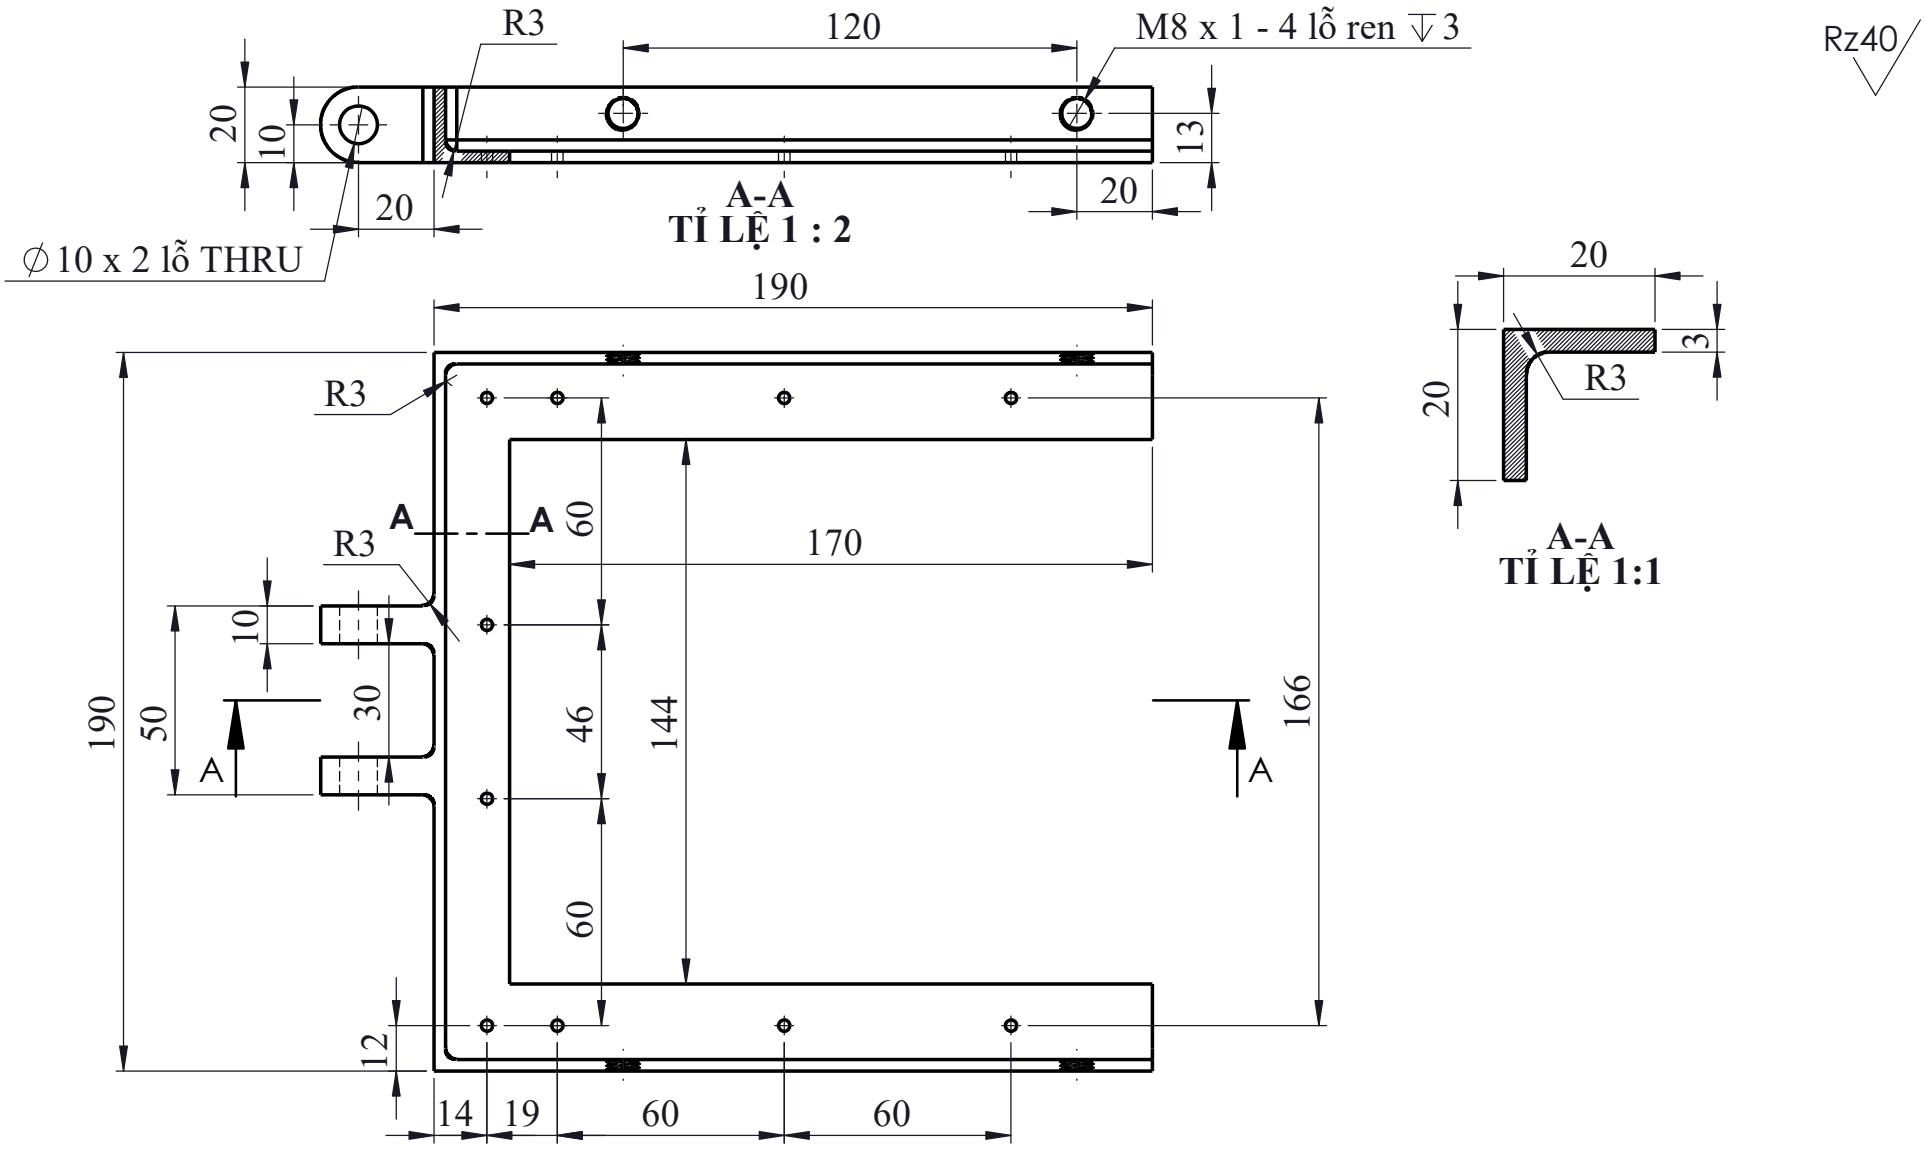


Người vẽ			**KHUNG SÀNG 1**
Kiểm tra			
Trường Đại học Công nghiệp Thành phố Hồ Chí Minh Khoa Cơ Khí		THÉP V 20X20X3	Tỉ lệ 1:2 SL:01