

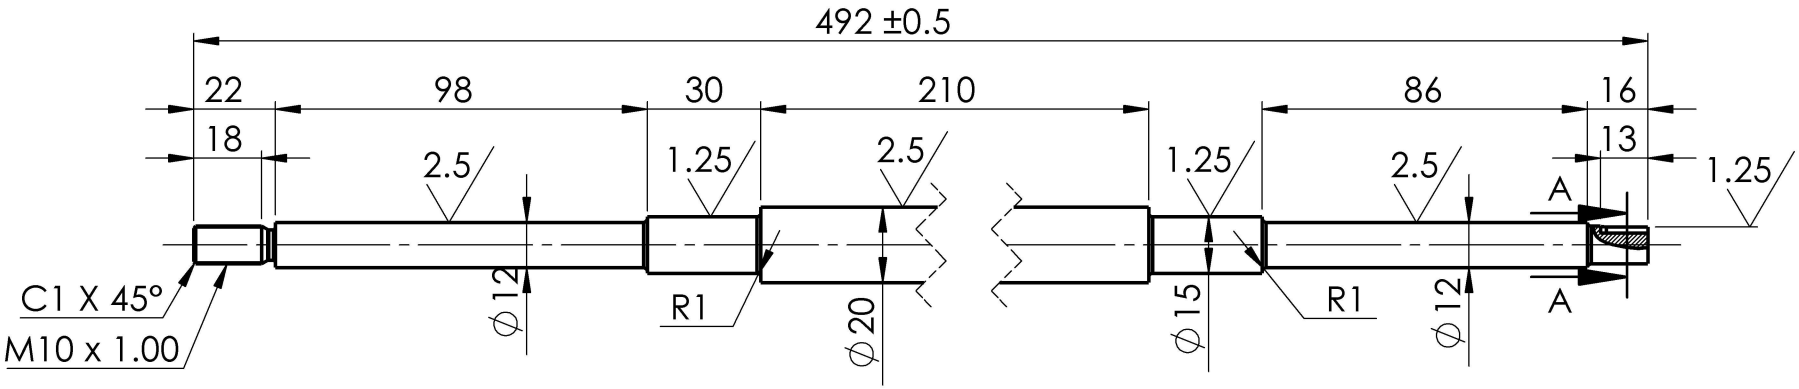


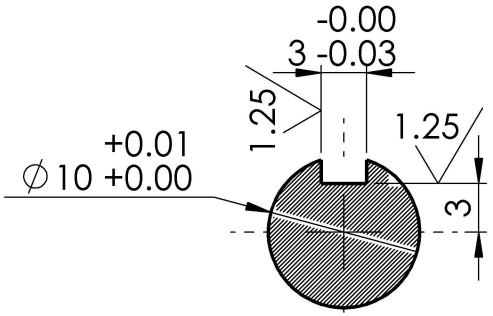

A-A
TỈ LỆ 2 : 1

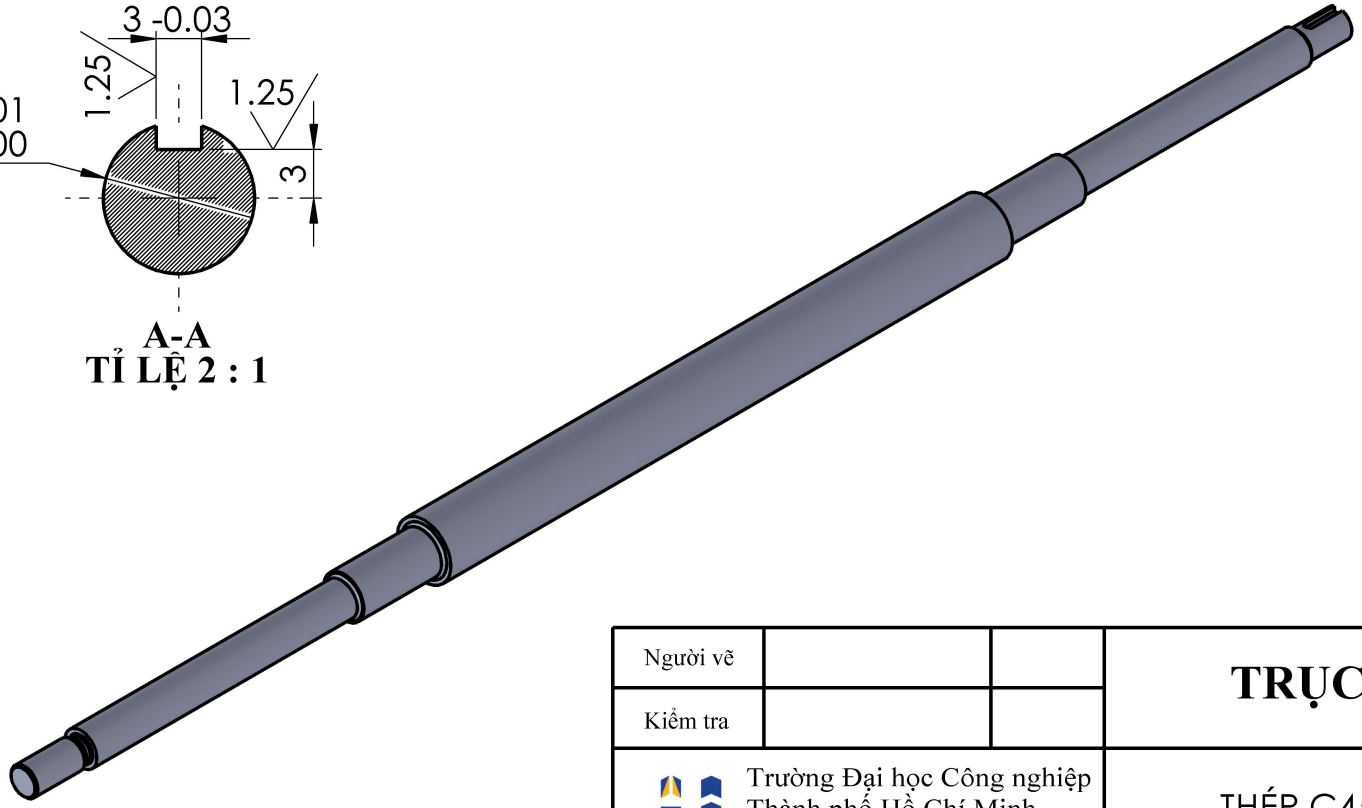

Người vẽ			**TRỤC SÀNG 2**
Kiểm tra			
Trường Đại học Công nghiệp Thành phố Hồ Chí Minh Khoa Cơ Khí		THÉP C45	Tỉ lệ 1:2 SL:01