
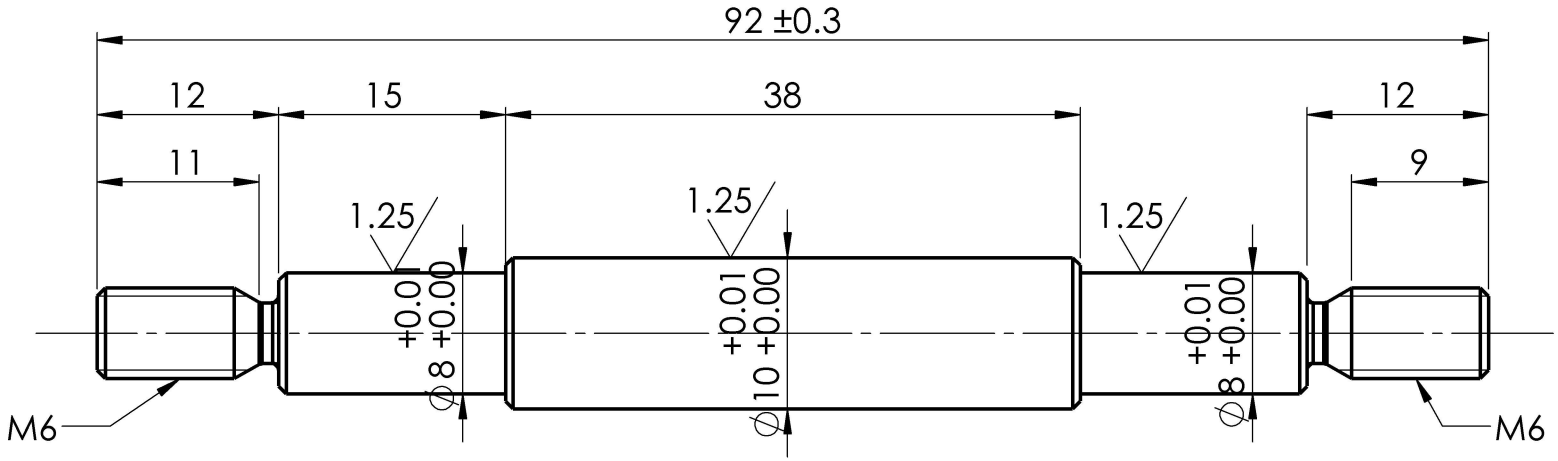


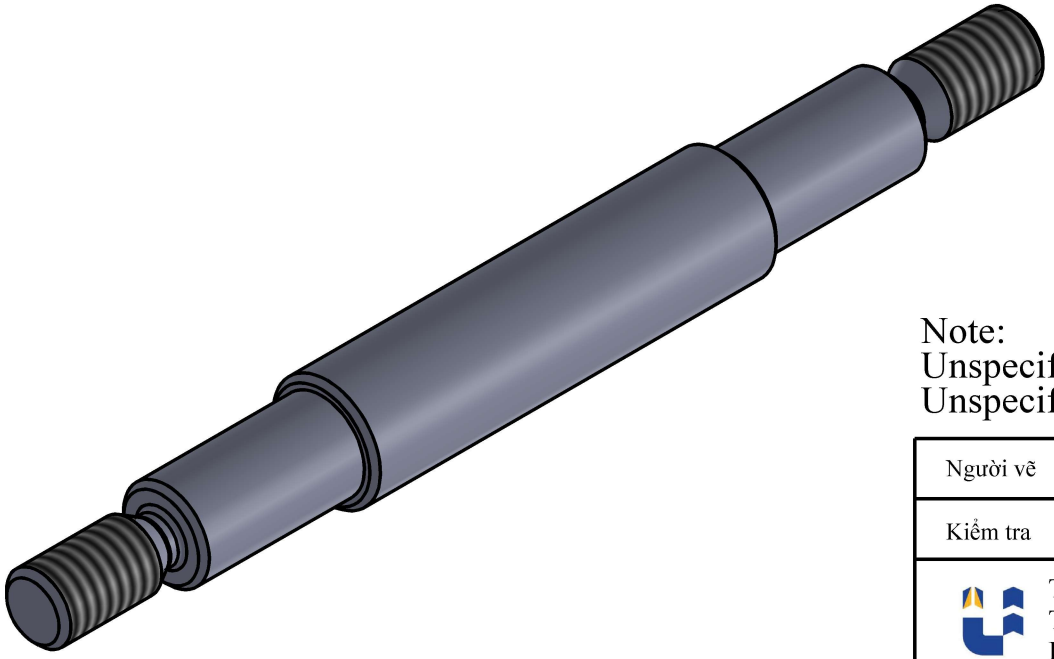

Note:
Unspecified chamfer 0,5 x 45
Unspecified radius 1

Người vẽ			**TRỤC LẮP THANH TRUYỀN**
Kiểm tra			
Trường Đại học Công nghiệp Thành phố Hồ Chí Minh Khoa Cơ Khí		THÉP C45	Tỉ lệ 2:1 SL:01